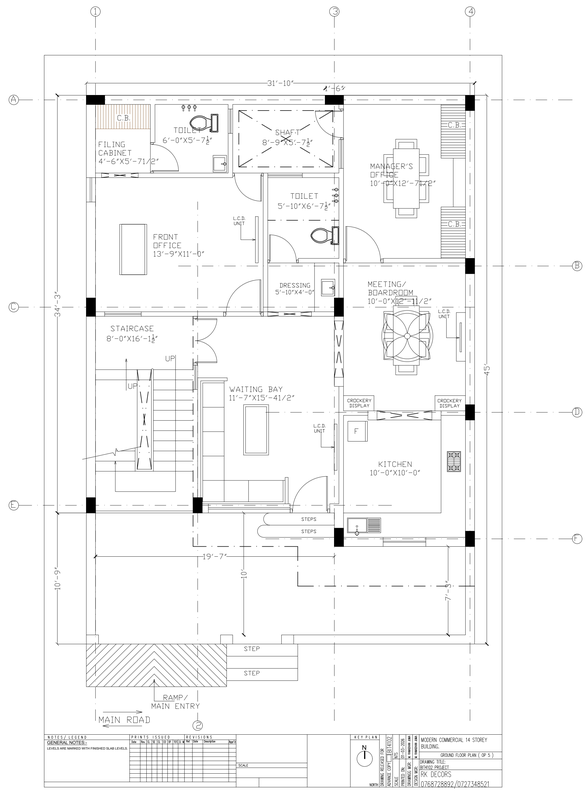

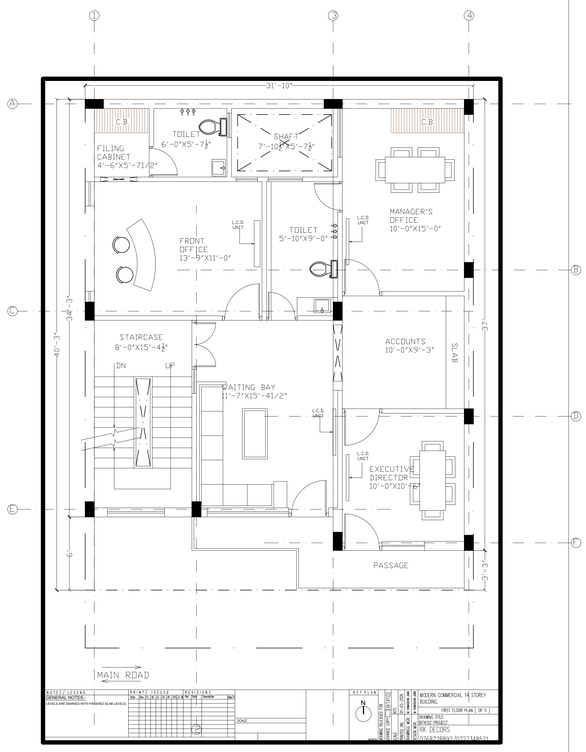

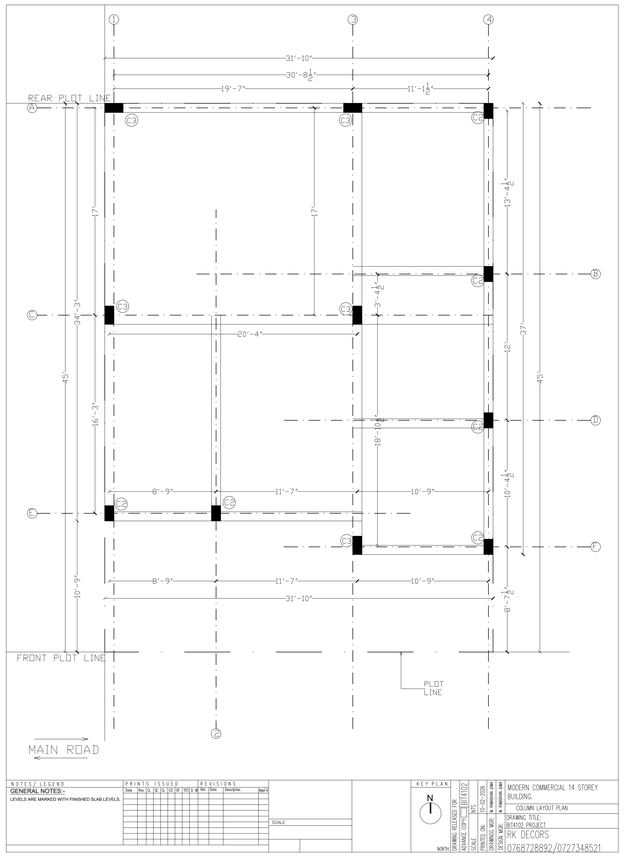

FINAL PLAN

(First floor layout applys to all remaining floors)

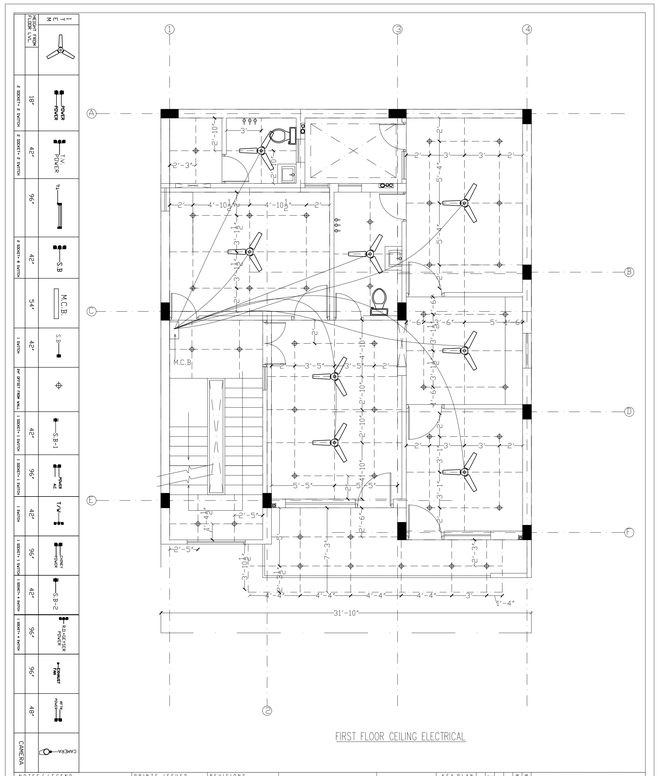
FIRST FLOOR CEILING ELECTRICAL
31'-10"
M.C.B.
NOTES / LEGEND
GENERAL NOTES:-
LEVELS ARE MARKED WITH FINISHED SLAB LEVELS.
PRINTS ISSUED
REVISIONS
KEY PLAN
MODERN COMMERCIAL 14 STOREY BUILDING.
FIRST FLOOR CEILING ELECTRICAL PLAN
DRAWING TITLE:
BT8202 PROJECT.
RK DECORS
07687728892/07273348521

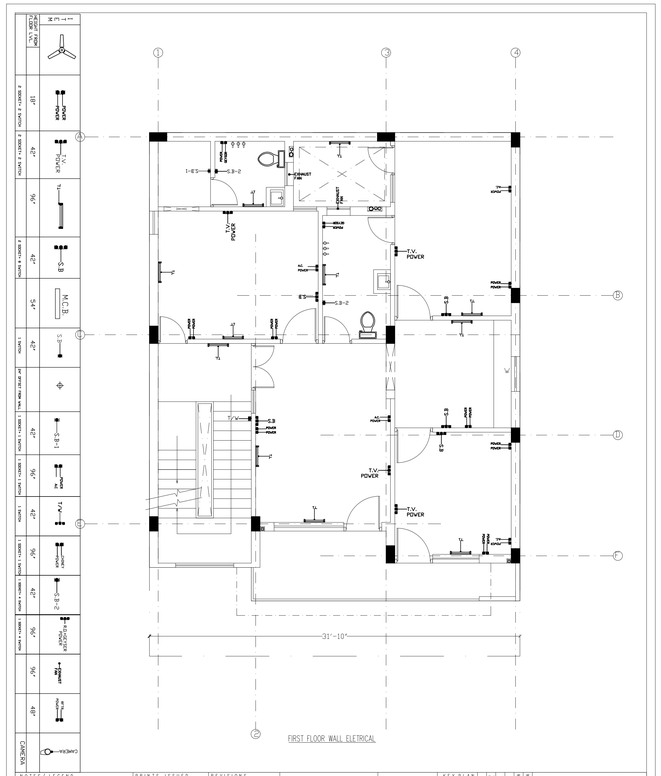
FIRST FLOOR WALL ELETRICAL
31'-10"
T.V. POWER
EXHAUST FAN
NOTES / LEGEND
GENERAL NOTES:-
LEVELS ARE MARKED WITH FINISHED SLAB LEVELS.
PRINTS ISSUED
REVISIONS
KEY PLAN
MODERN COMMERCIAL 14 STOREY BUILDING.
FIRST FLOOR WALL ELECTRICAL PLAN
DRAWING TITLE:
BT8202 PROJECT.
RK DECORS
07687728892/07273348521

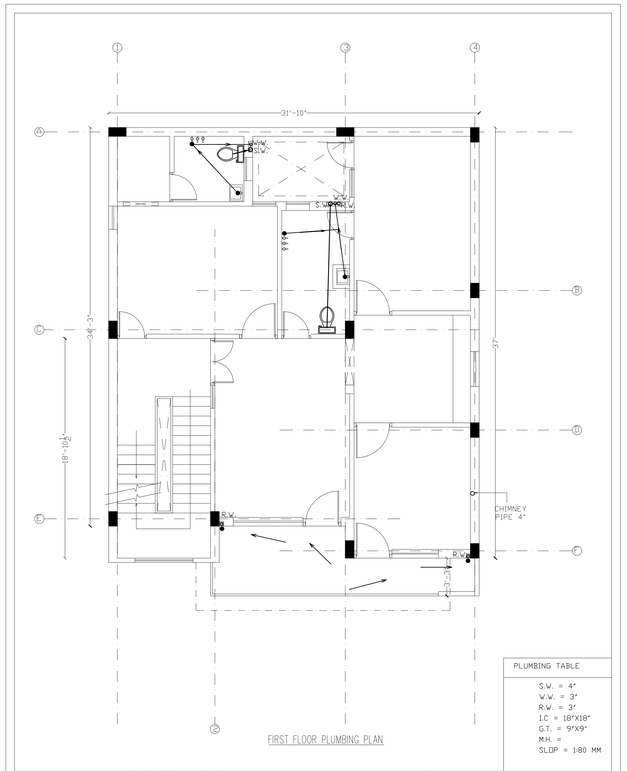
FIRST FLOOR PLUMBING PLAN
31'-10"
CHIMNEY PIPE 4"
PLUMBING TABLE
S.W. = 4"
W.W. = 3"
R.W. = 3"
I.C = 18"X18"
G.T. = 9"X9"
M.H. = 9"X9"
SLOP = 1:80 MM
NOTES / LEGEND
GENERAL NOTES:-
LEVELS ARE MARKED WITH FINISHED SLAB LEVELS.
PRINTS ISSUED
REVISIONS
KEY PLAN
MODERN COMMERCIAL 14 STOREY BUILDING.
FIRST FLOOR PLUMBING PLAN
DRAWING TITLE:
BT8202 PROJECT.
RK DECORS
07687728892/07273348521

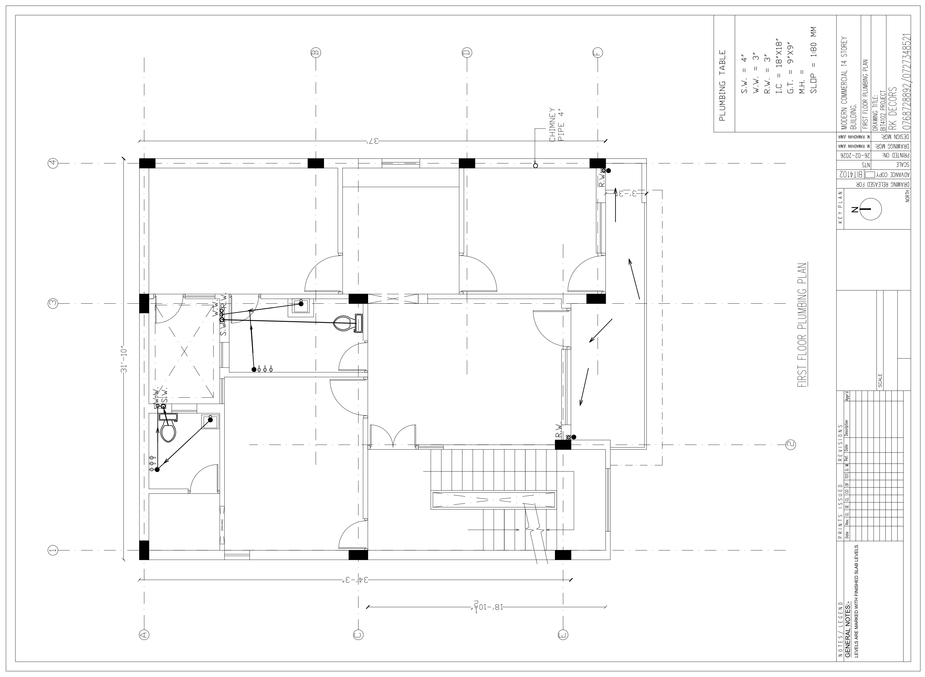
FIRST FLOOR PLUMBING PLAN
PLUMBING TABLE
S.V. = 4"
V.V. = 3"
R.V. = 3"
I.C = 18"X18"
G.T. = 9"X9"
W.V. = 3"
SLOP = 1:80 MM
CHIMNEY PIPE 4"
77'
31'-10"
34'-3"
18'-10½"
R.V.
V.V.
S.V.
MODERN COMMERCIAL 14 STOREY BUILDING.
FIRST FLOOR PLUMBING PLAN
DRAWING TITLE
ARCHITECT
RK DECORS
07687278892/07273348521
DRAWING NO.
DATE 24-02-2026
SCALE NTS
DRAWING RELEASED FOR
GENERAL NOTES:

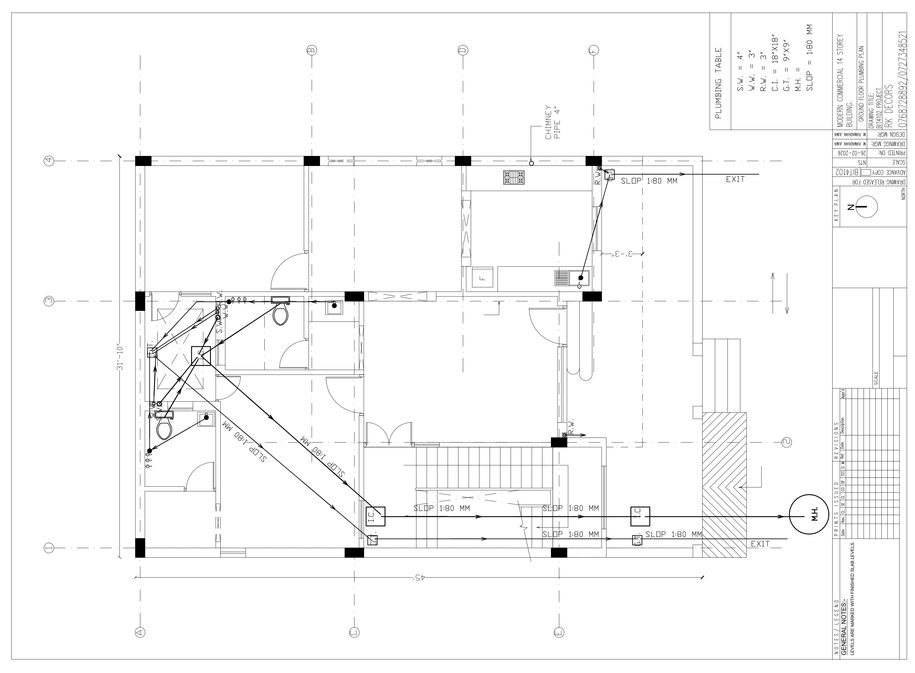
GROUND FLOOR PLUMBING PLAN
PLUMBING TABLE
S.V. = 4"
V.V. = 3"
R.V. = 3"
C.I. = 18"X18"
G.T. = 9"X9"
W.V. = 3"
SLOP = 1:80 MM
CHIMNEY PIPE 4"
SLOP 1:80 MM
EXIT
M.H.
45'
31'-10"
MODERN COMMERCIAL 14 STOREY BUILDING.
GROUND FLOOR PLUMBING PLAN
DRAWING TITLE
ARCHITECT
RK DECORS
07687278892/07273348521
DRAWING NO.
DATE 24-02-2026
SCALE NTS
DRAWING RELEASED FOR
GENERAL NOTES:

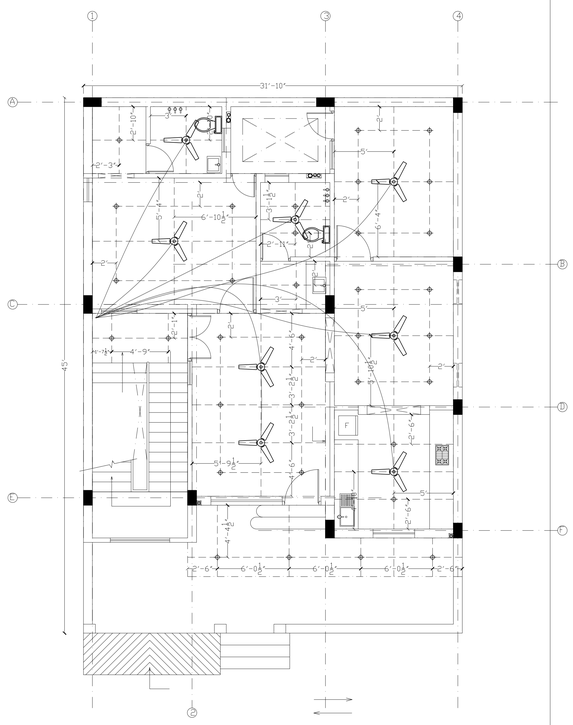

NOTES / LEGEND

GENERAL NOTES:-

LEVELS ARE MARKED WITH FINISHED SLAB LEVELS.

PRINTS ISSUED						REVISIONS			
Date	Dwg.	CL	DB	DL	DD	DP	TECH.	Ref.	Date	Description	Sign

SCALE

KEY PLAN

N

NORTH

DRAWING RELEASED FOR:
GENERAL COMPLIANCE
SCALE:
DATE: 25-02-2026
PROJECT No.: 0814102
DRAWN BY: AB
CHECKED BY: RK

MODERN COMMERCIAL 14 STOREY BUILDING.

GROUND FLOOR CEILING ELECTRICAL PLAN

DRAWING TITLE:

0814102 PROJECT.

RK DECORS

0768728892/0727348521

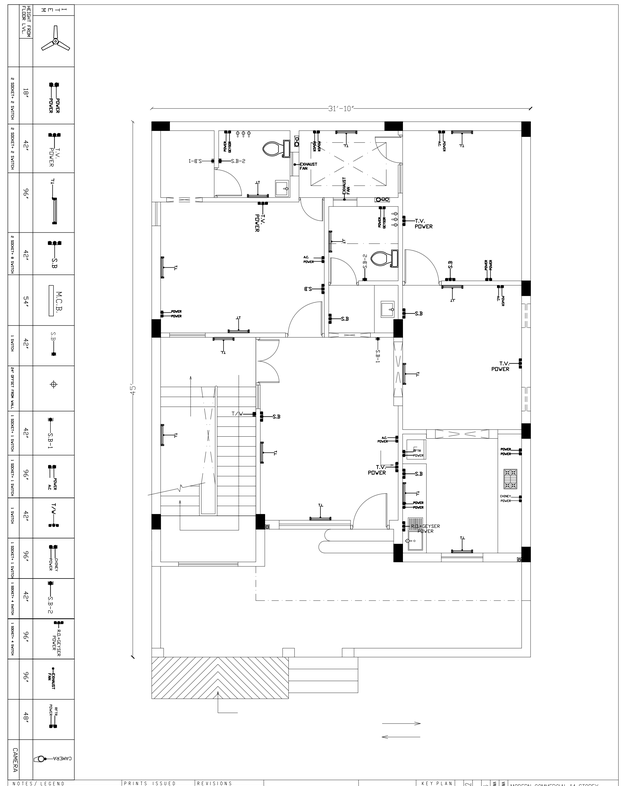
31'-10"
45'
T.V. POWER
T.V. POWER
T.V. POWER
T.V. POWER
T.V.
EXHAUST FAN
EXHAUST FAN
EXHAUST FAN
AC POWER
AC POWER
AC POWER
POWER
POWER